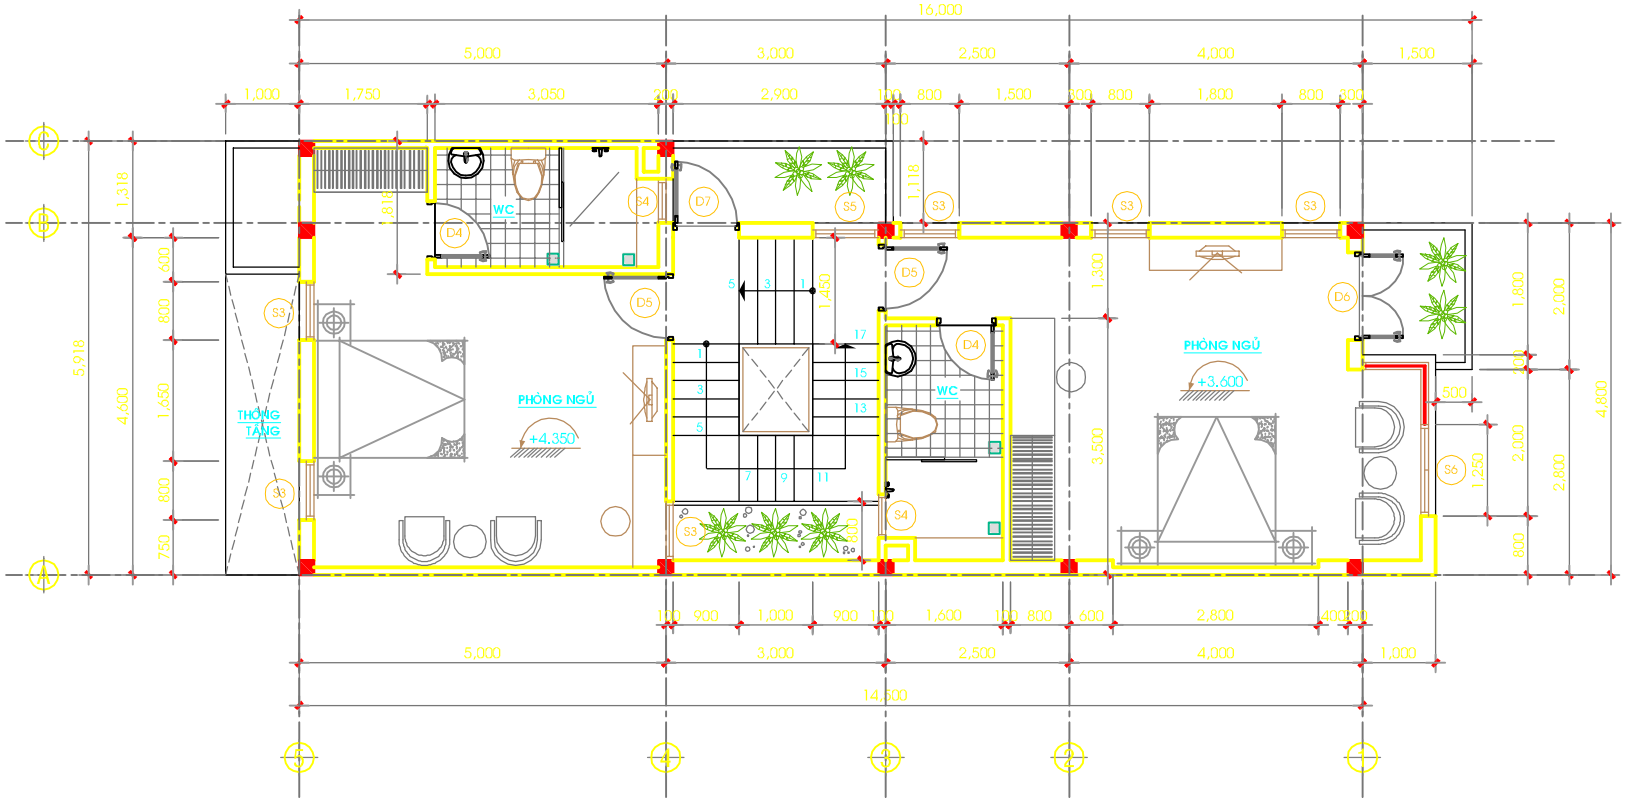

MẶT BẰNG LẦU 1

TL : 1/50

D.SÀN PHÒNG NGỦ :

- LÁT SÀN GỖ
- LỚP VỮA XM MÁC 100 , DÀY 20
- LỚP ĐAN B.T.C.T(XEM BẢN VẼ KẾT CẤU)
- LỚP VỮA TÔ
- TRẦN THẠCH CAO
- SƠN NƯỚC

E.SÀN BAN CÔNG :

- LÁT GẠCH CERAMIC 40x40 (MS : .....)
- LỚP VỮA XM MÁC 100 , DÀY 15,DỐC 2% VỀ PHÍA PHỄU THU
- LỚP BÊ TÔNG GẠCH VỠ
- LỚP CHỐNG THẤM QUÉT TRÊN BỀ MẶT BÊTÔNG
- LỚP ĐAN B.T.C.T(XEM BẢN VẼ KẾT CẤU)
- LỚP VỮA TÔ
- SƠN NƯỚC

F.SÀN VỆ SINH LẦU :

- LÁT GẠCH CERAMIC NHÁM 25x25 (MS:.....)
- LỚP VỮA XM MÁC 100 , DÀY 15,DỐC 2% VỀ PHÍA PHỄU THU
- LỚP CHỐNG THẤM QUÉT TRÊN BỀ MẶT BÊTÔNG
- LỚP ĐAN B.T.C.T(XEM BẢN VẼ KẾT CẤU)
- LỚP VỮA TÔ
- TRẦN THẠCH CAO CHỐNG ẨM
- SƠN NƯỚC